



Glenda Place

Plumpton, NSW | Residential addition | Resolved exterior study

Private client, title-block and approval records omitted.


DRAWING LIST			
Sheet Number	Sheet Name	Current Revision Description	Current Revision
A01	PERSPECTIVE	FOR CDC	2
A02	AUSTRALIAN STANDARD	FOR CDC	3
A03	SITE DEVELOPMENT PLAN	FOR CDC	4
A04	EXISTING FLOOR PLAN	FOR CDC	1
A05	DEMOLITION FLOOR PLAN	FOR CDC	1
A06	FLOOR PLAN	FOR CDC	4
A07	ROOF PLAN	FOR CDC	2
A08	ELEVATION	FOR CDC	1
A09	ELEVATION & SECTION	FOR CDC	2
A10	DOOR & WINDOW SCHEDULE	FOR CDC	2
A11	LIGHTING LAYOUT	FOR CDC	2
A12	POWER LAYOUT	FOR CDC	1
A13	ISOMETRIC	FOR CDC	1
A14	CONCRETE PROFILE LAYOUT	FOR CDC	2
A15	DOOR THRESHOLD DETAIL & WINDOW DETAIL	FOR CDC	2
A16	BASIX COMMITMENT PLAN	FOR CDC	2
A17	CONDENSATION MANAGEMENT PLAN	FOR CDC	1
A18	ARTICULATION JOINT DETAIL	FOR CDC	1


SITE CALCULATION :SEPP 2008	
TOTAL LAND AREA	564.60 SQM
SITE AREA	
PROPOSED FLOOR AREA (GFA)	176.00 SQM
GARAGE	33.50 SQM
TOTAL SITE COVERAGE	209.50 SQM
LANDSCAPE AREA	238.16 SQM
SITE COVERAGE	
ALLOWED SITE COVERAGE FOR ALL BUILDINGS 25% + 150	291.15 SQM
LANDSCAPING	
MINIMUM LANDSCAPE AREA 50% OF TOTAL SITE AREA - 100	182.30 SQM
LANDSCAPE AREA PROPOSED LANDSCAPE AREA 42% OF ALL SITE AREA	238.16 SQM
MIN LANDSCAPE AREA BEHIND THE BUILDING LINE 50% OF REQUIRED LANDSCAPING AREA MIN 1.5 WIDTH AND LENGTH	79.050 SQM
LANDSCAPE AREA BEHIND THE FRONT BUILDING LINE	136.61 SQM
PRIVATE OPEN SPACE REQUIRED (MIN. DIMENSION 3M)	16.00 SQM
PRIVATE OPEN SPACE PROPOSED	30.00 SQM
LANDSCAPING	
DEEP SOIL LANDSCAPE FRONTYARD:	109.46 SQM
BACKYARD :	128.70 SQM
TOTAL DEEP SOIL LANDSCAPE:	238.16 SQM
PERMEABLE AREA INCLUDING DRIVE AND WALK WAY	55.45 SQM
PROPOSED LANDSCAPING AREA 42% OF TOTAL SITE	238.16 SQM



2 EXTERIOR PERSPECTIVE 2



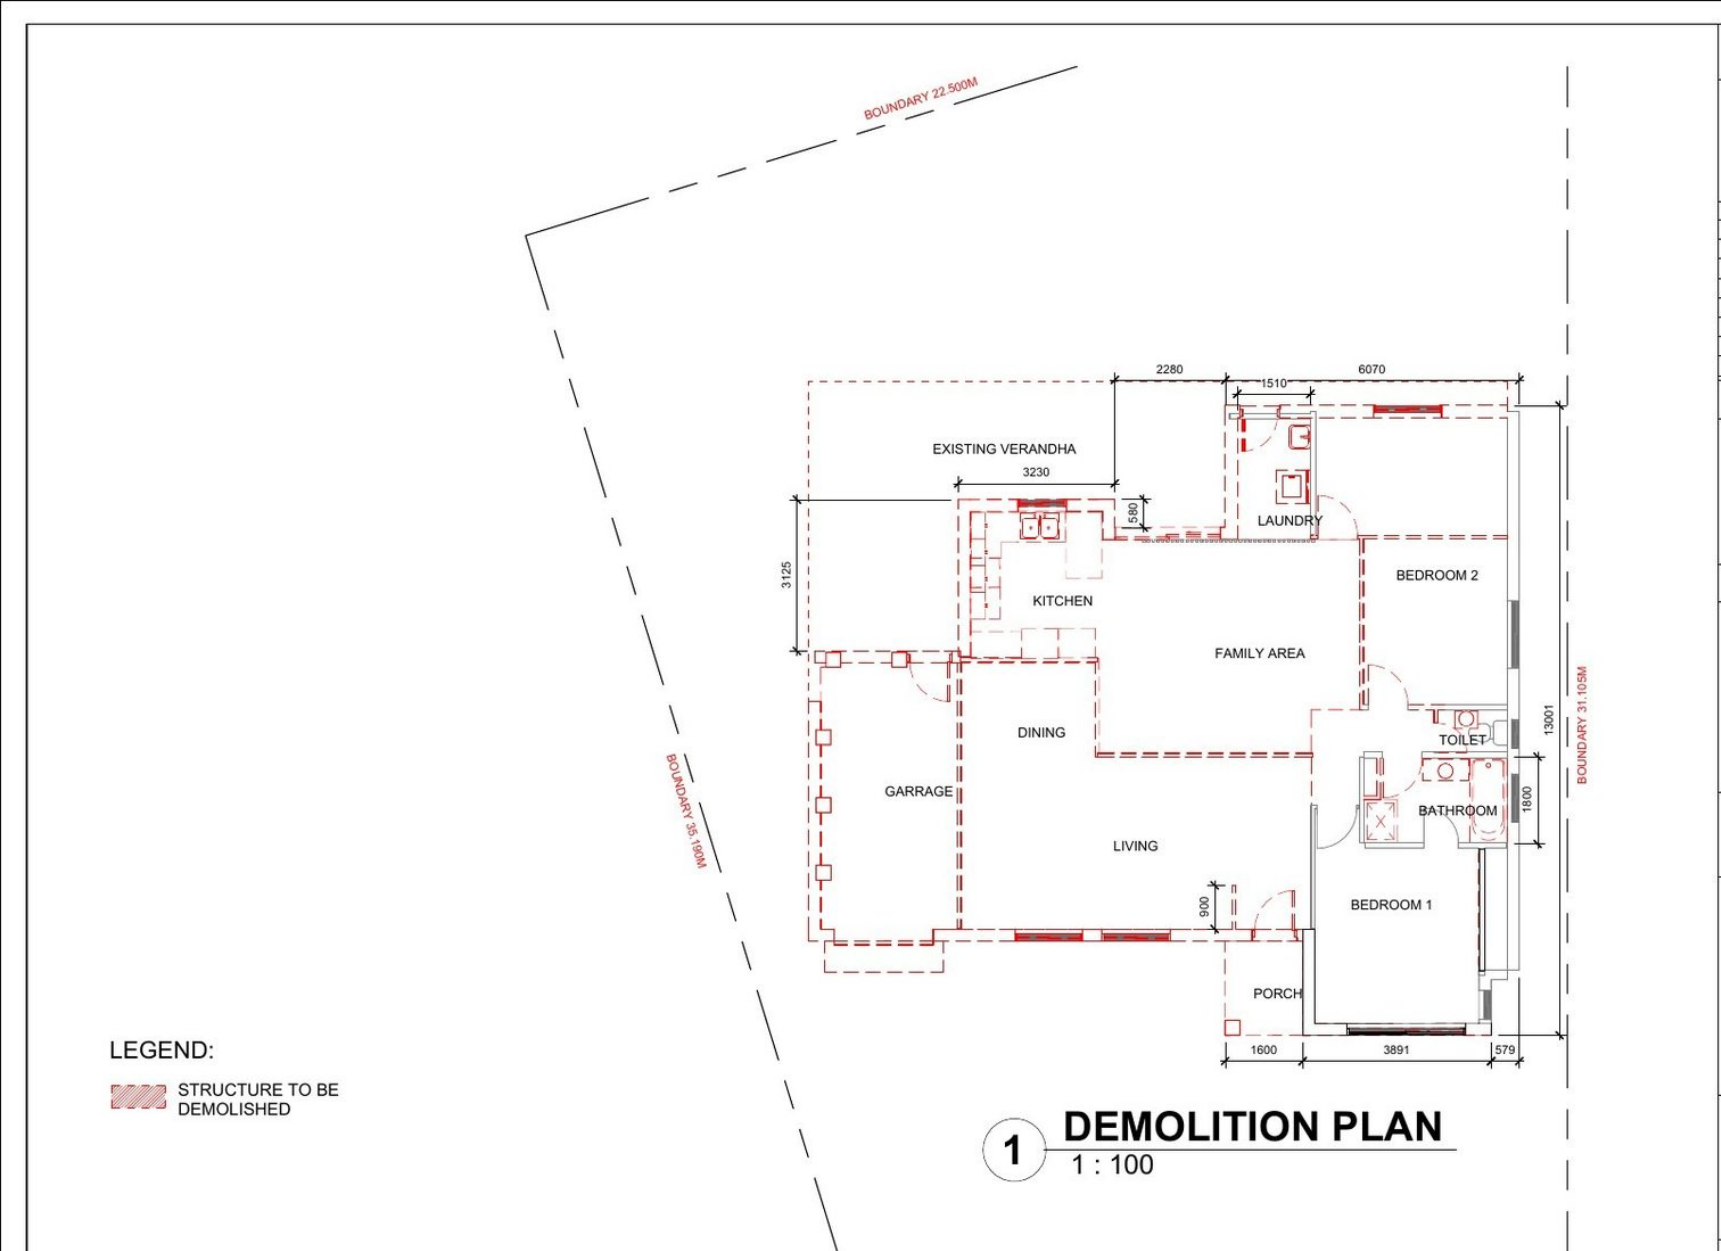

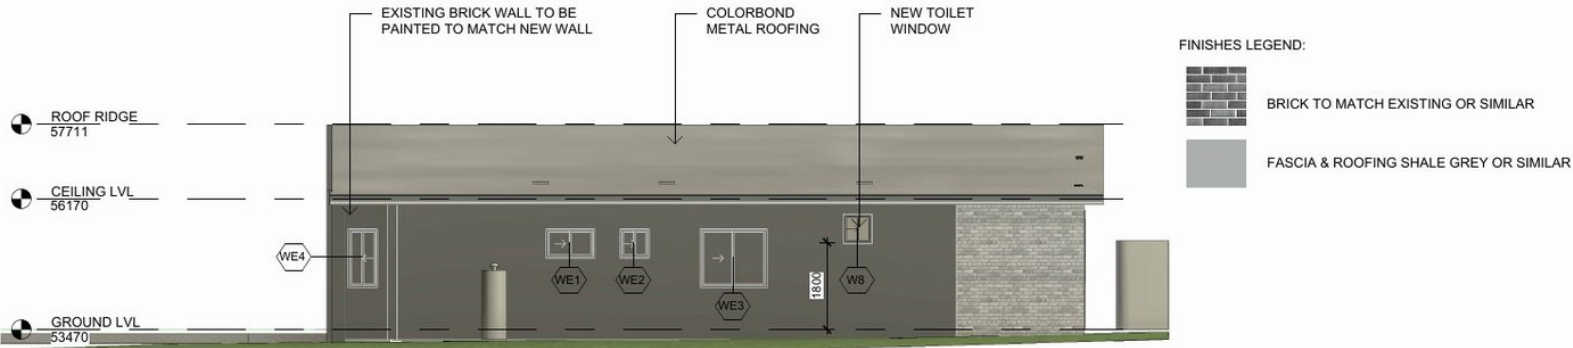

1 WEST ELEVATION
1 : 100



2 CROSS SECTION
1 : 100

